



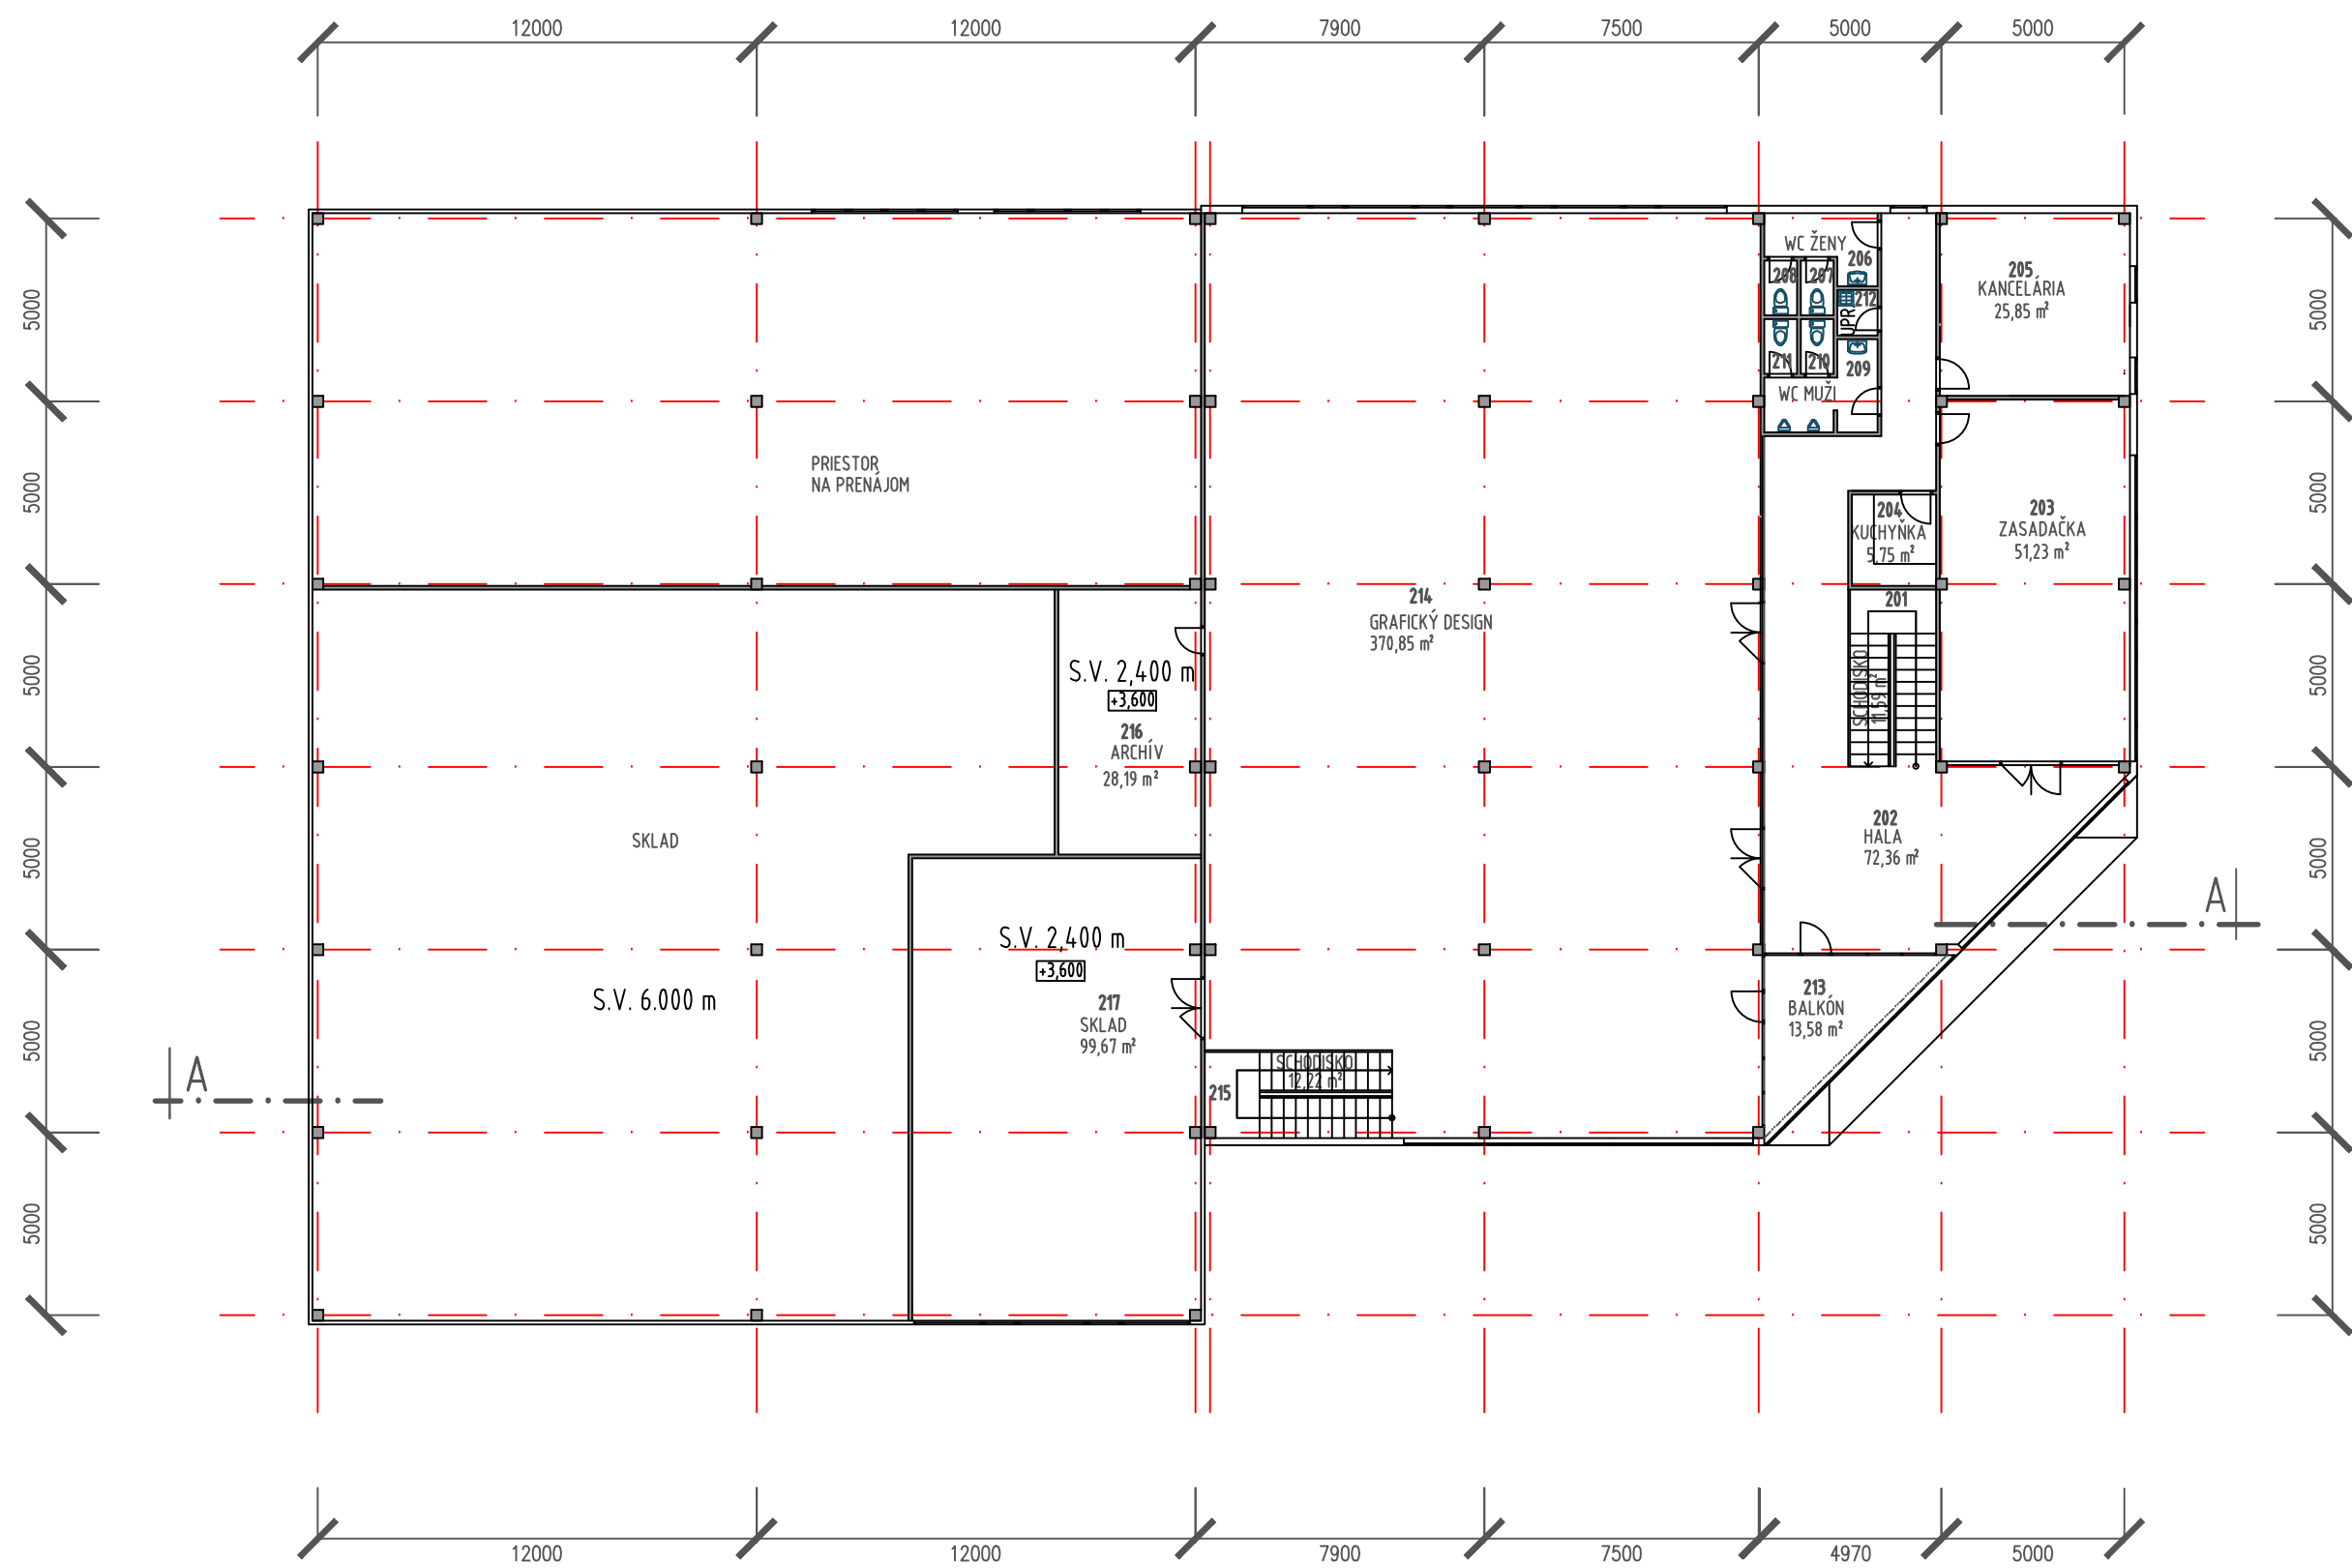

Pôdorys 2. NP

ČÍSLO M.	NÁZOV MIESTNOSTI	PLOCHA MIESTN.
201	SCHODISKO	11,59 m²
202	HALA	72,36 m²
203	ZASADAČKA	51,23 m²
204	KUCHYŇKA	5,75 m²
205	KANCELÁRIA	25,85 m²
206	PREDSEŇ WC ŽENY	4,60 m²
207	WC ŽENY	1,35 m²
208	WC ŽENY	1,35 m²
209	PREDSEŇ WC MUŽI	5,75 m²
210	WC MUŽI	1,35 m²
211	WC MUŽI	1,35 m²
212	UPRATOVAČKA	1,38 m²
213	BALKÓN	13,58 m²
214	GRAFICKÝ DESIGN	370,85 m²
215	SCHODISKO	12,22 m²
216	ARCHIV	28,19 m²
217	SKLAD	99,67 m²

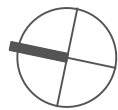

Pôdorys 2. N.P. 1:200

AREÁL FIRMY **SCRUB DESIGNZ**
NA PARCELE Č. 1130 - UL. BISKUPICKÁ V TREŇČINE
Investor: SCRUB DESIGNS, spol. s r. o., Ľudovíta Stárka 2152/16, 911 01 Trenčín
Architektonická štúdia - vypracoval: ArRea, spol. s r. o., Braneckého 8, 911 01 Trenčín
Autori: Ing. arch. Miloš Varga, Ing. arch. Miroslav Mlynček, dátum: marec 2026